




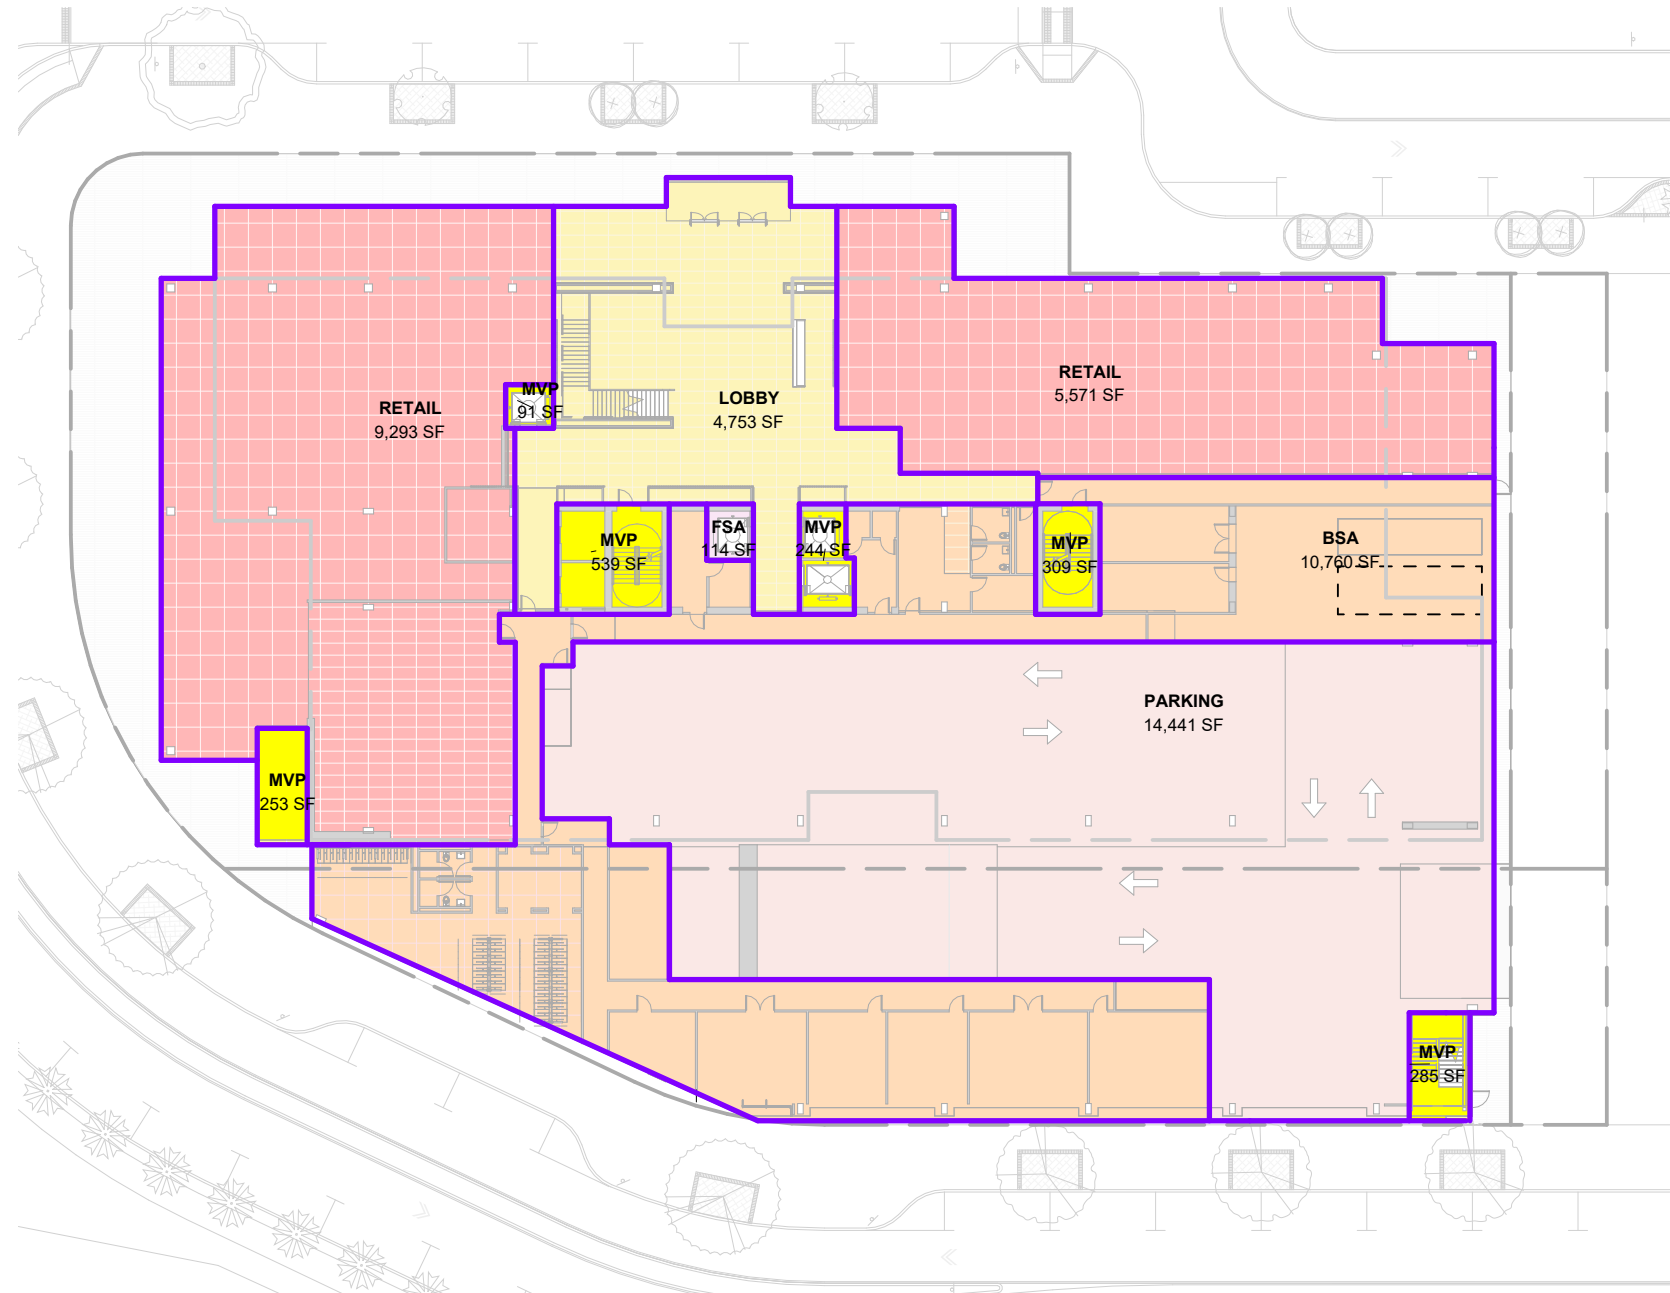


1 LEVEL 1 - LOBBY / RETAIL
1" = 40'-0"

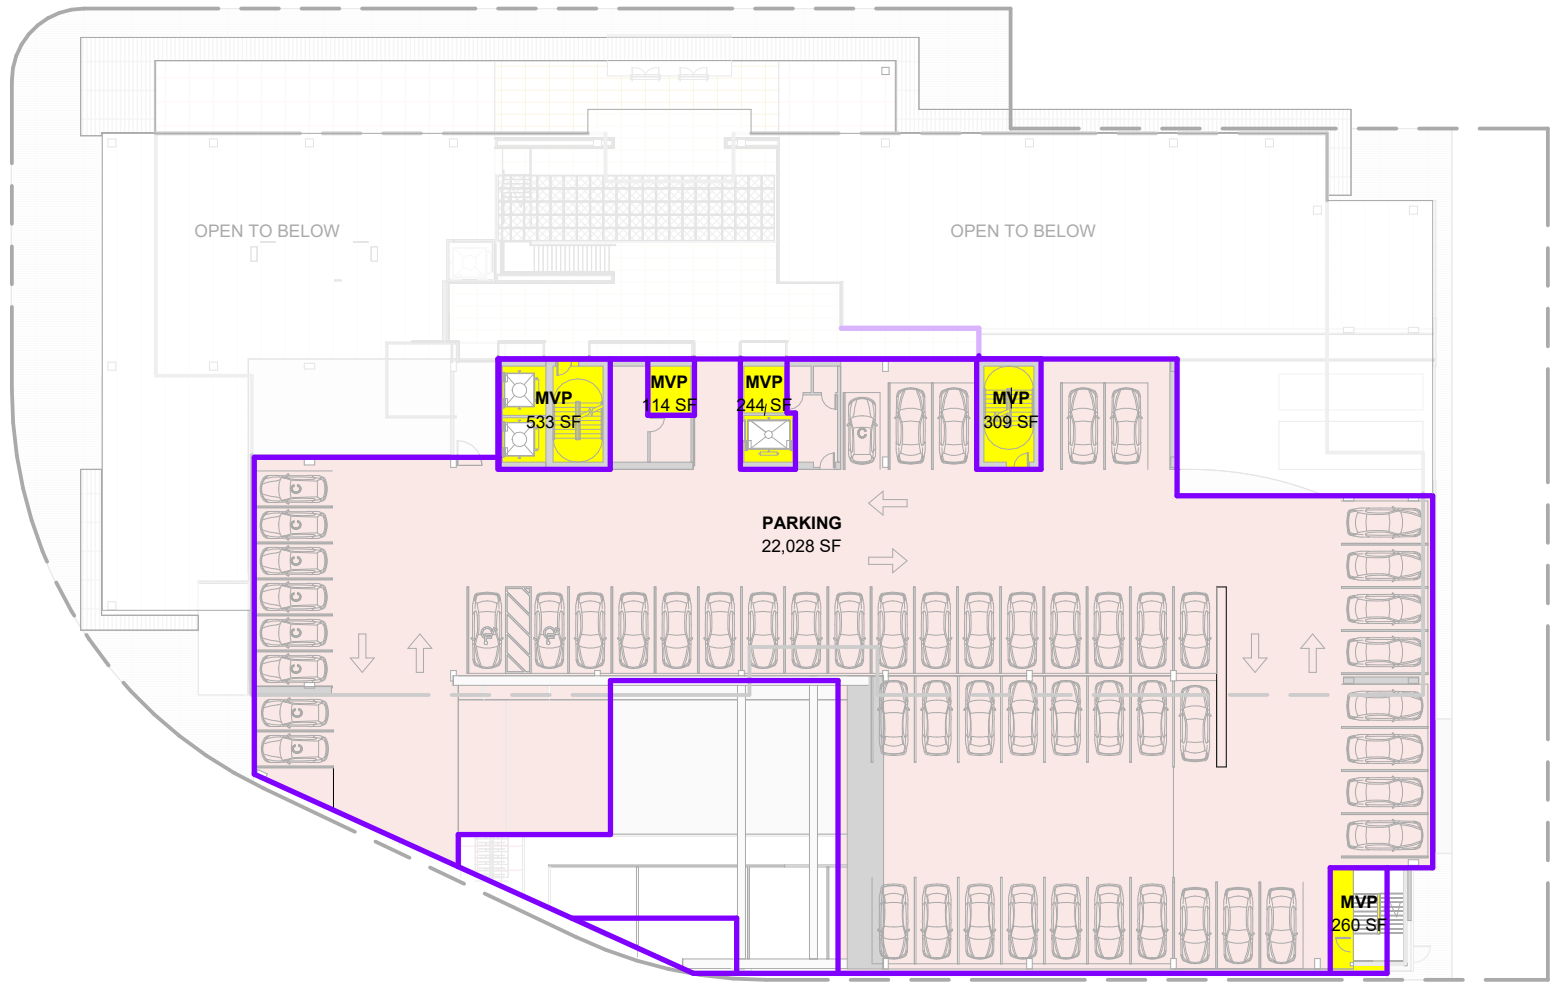


2 LEVEL 2 - PARKING
1" = 40'-0"

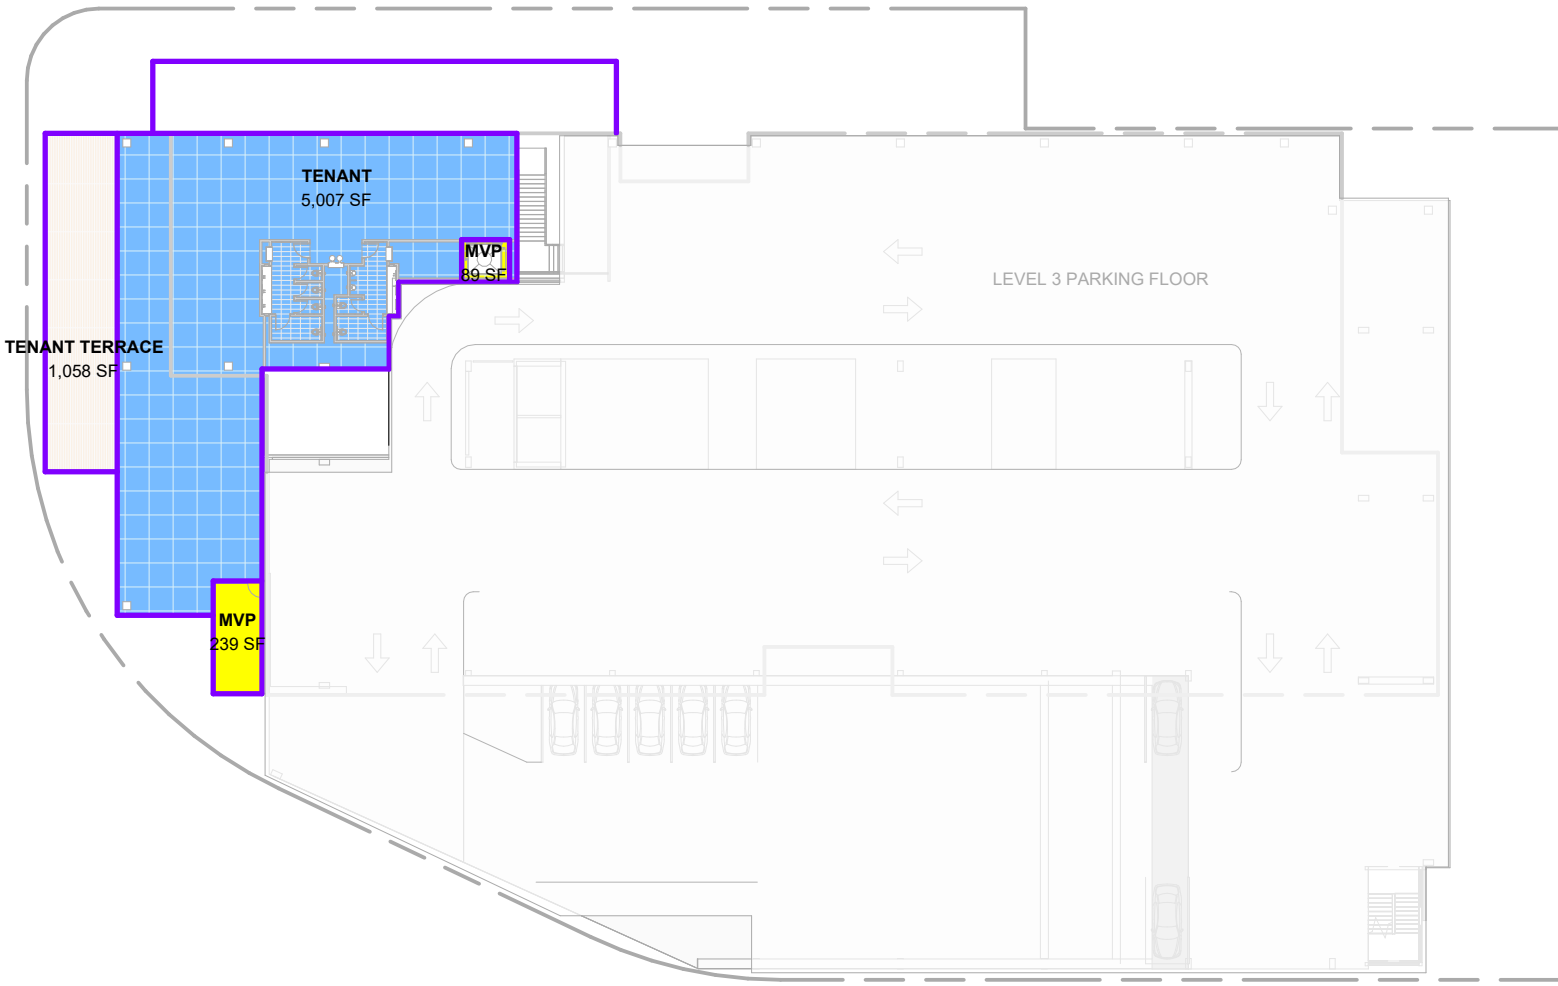


3 LEVEL 2 - OFFICE
1" = 40'-0"

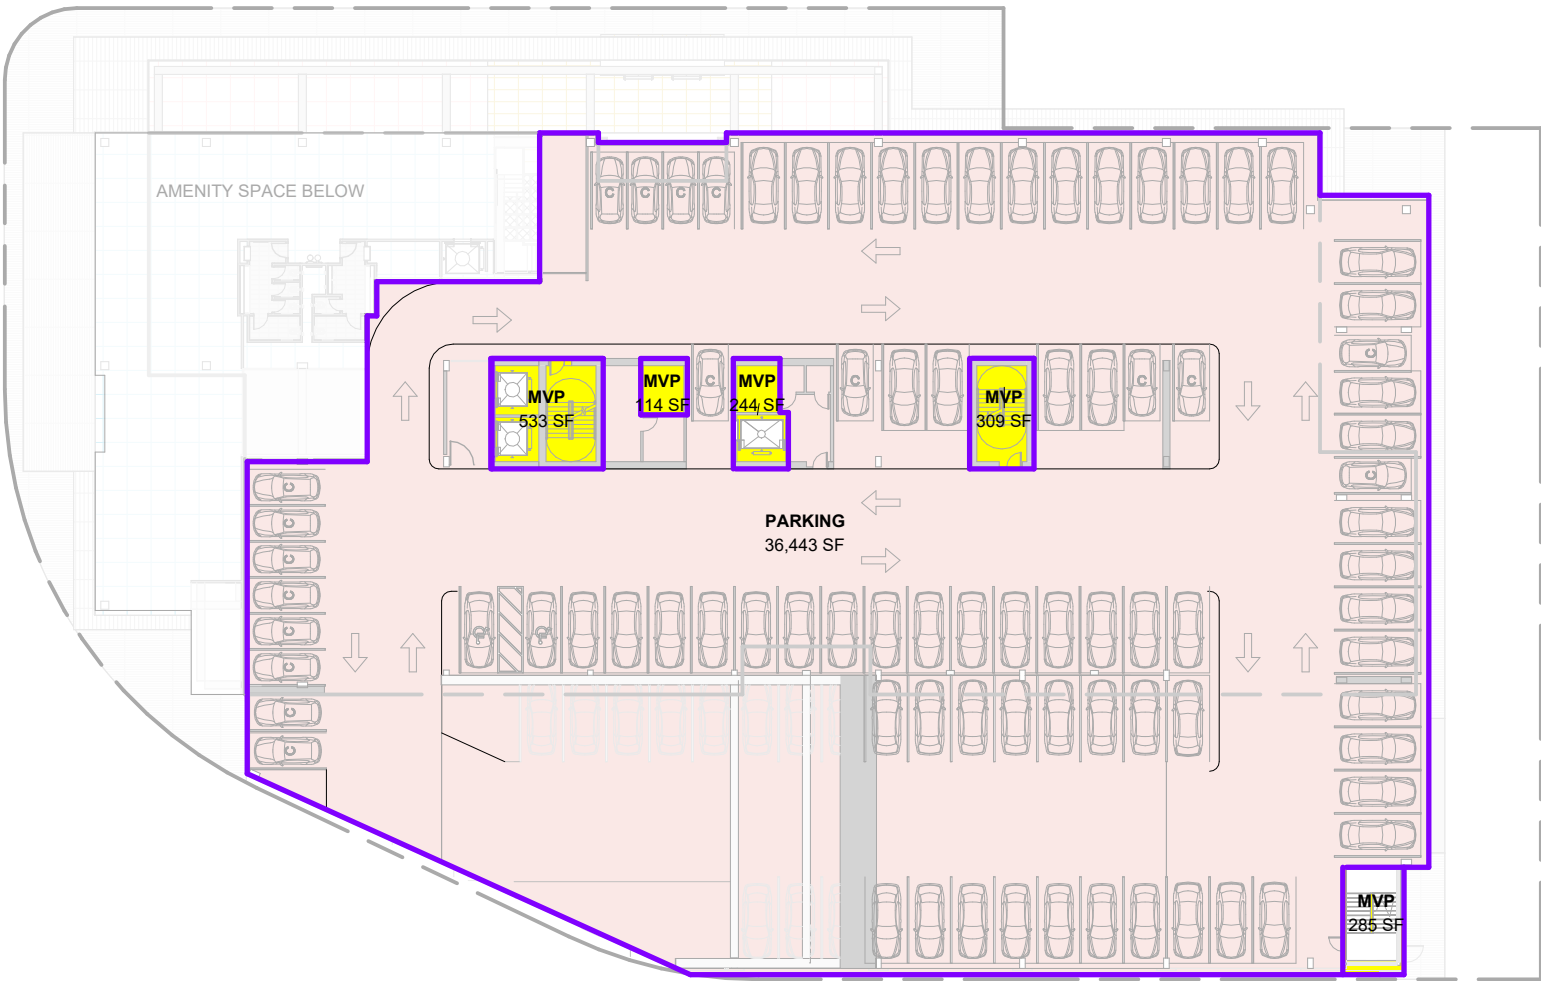


4 LEVEL 3 - PARKING
1" = 40'-0"

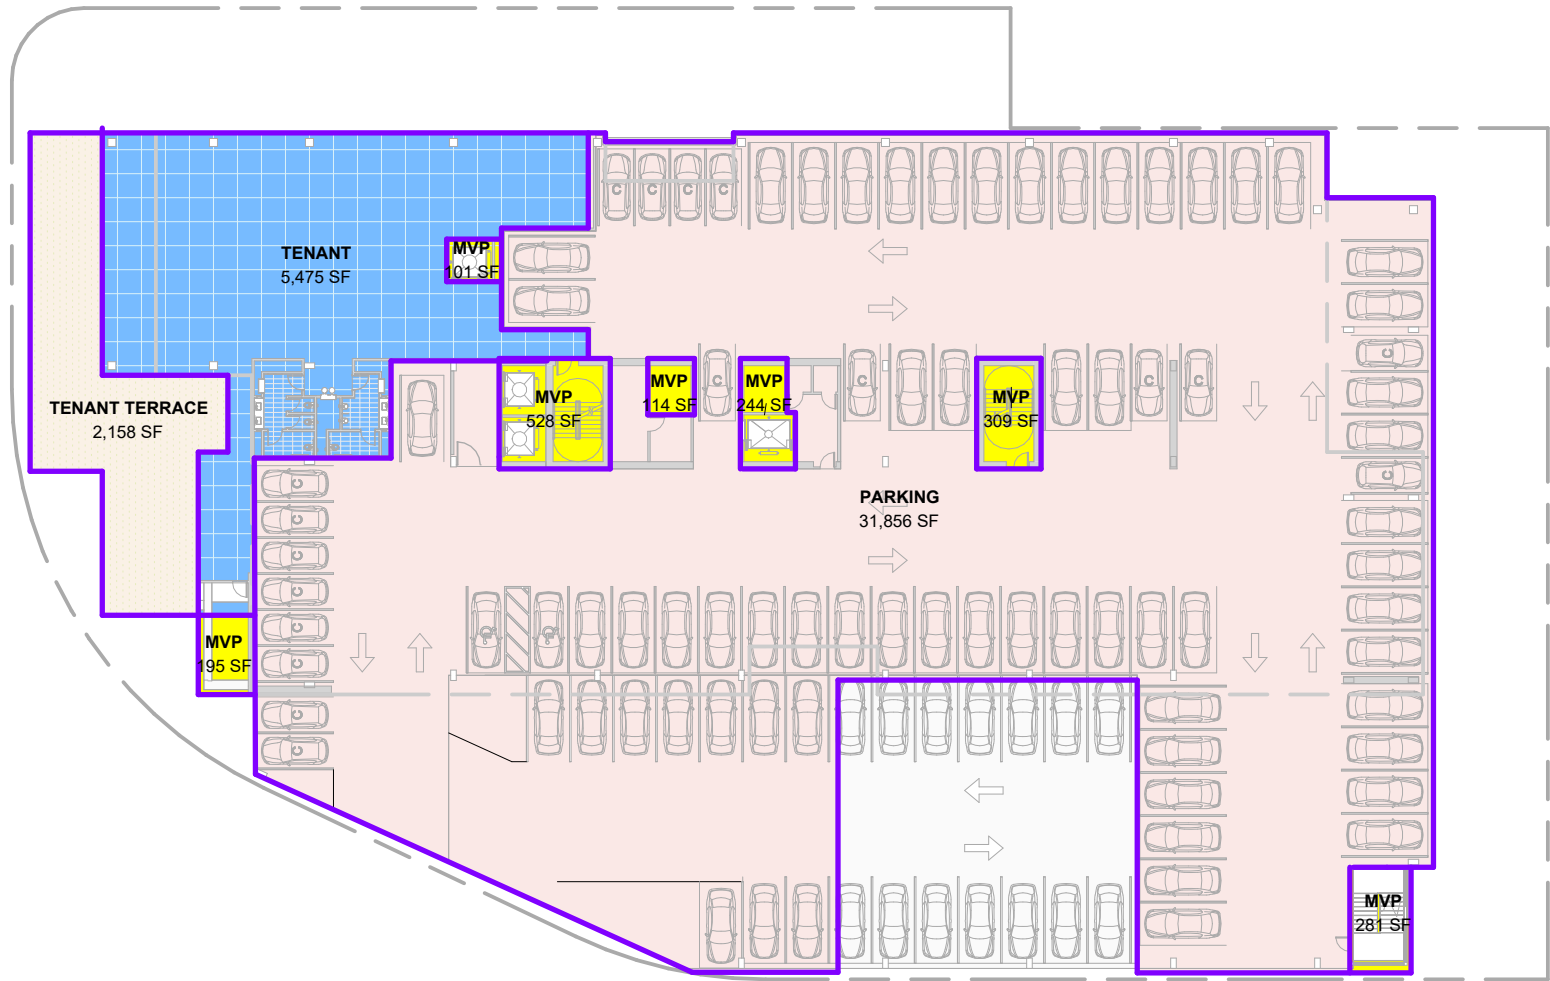


5 LEVEL 4 - PARKING
1" = 40'-0"

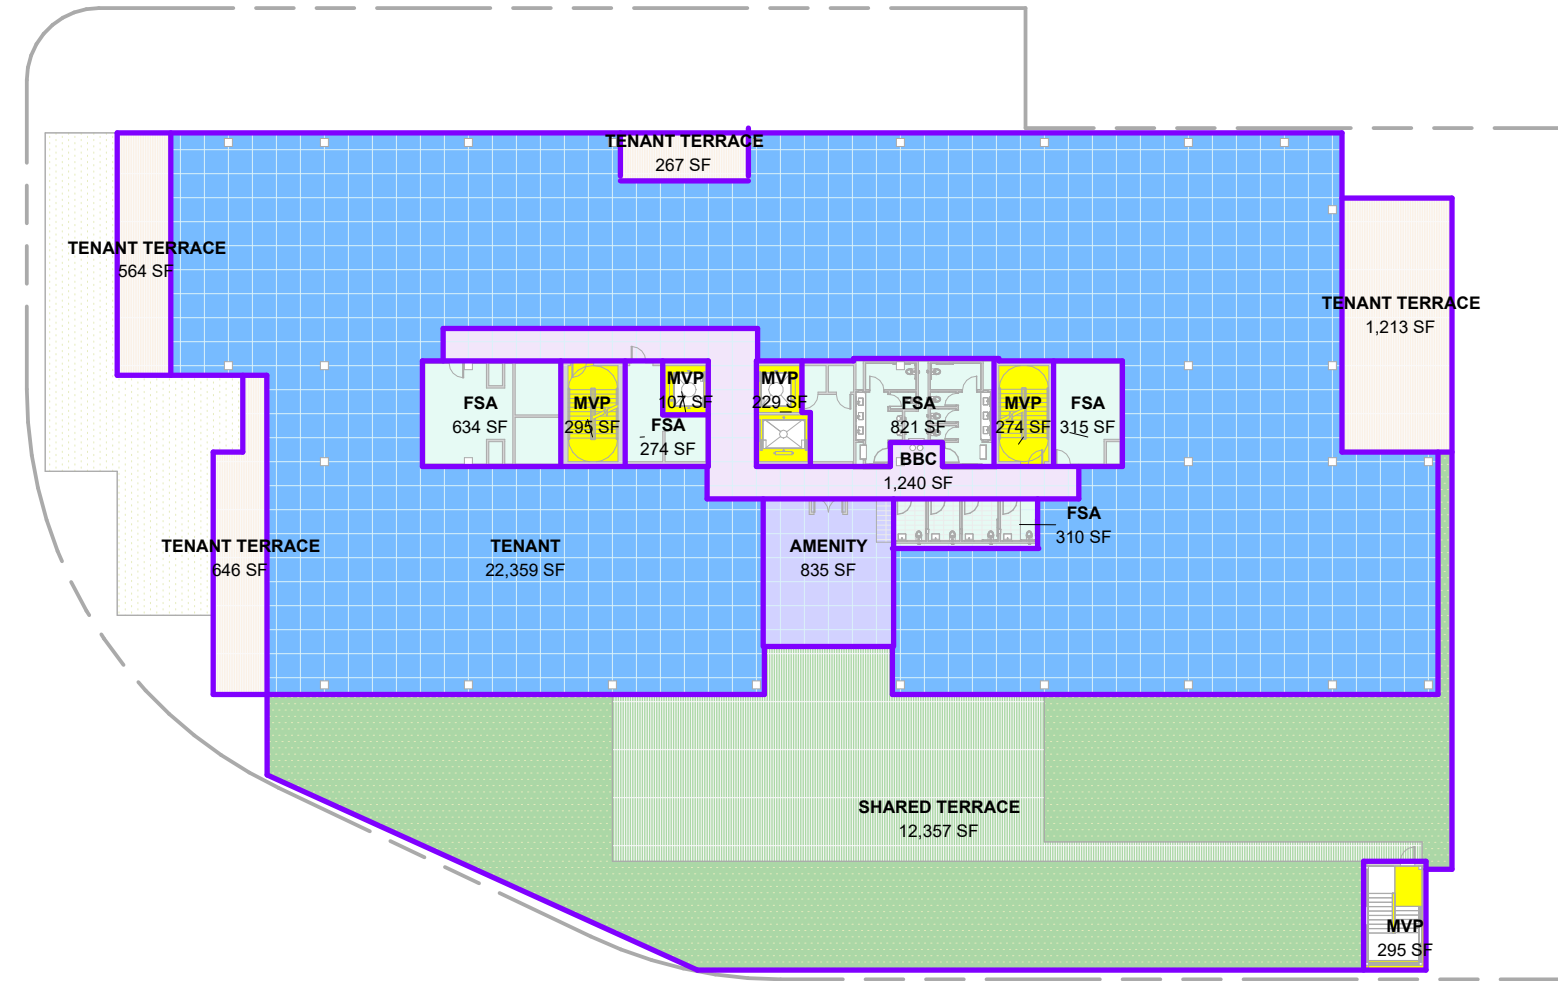

6 LEVEL 5 - OFFICE
1" = 40'-0"

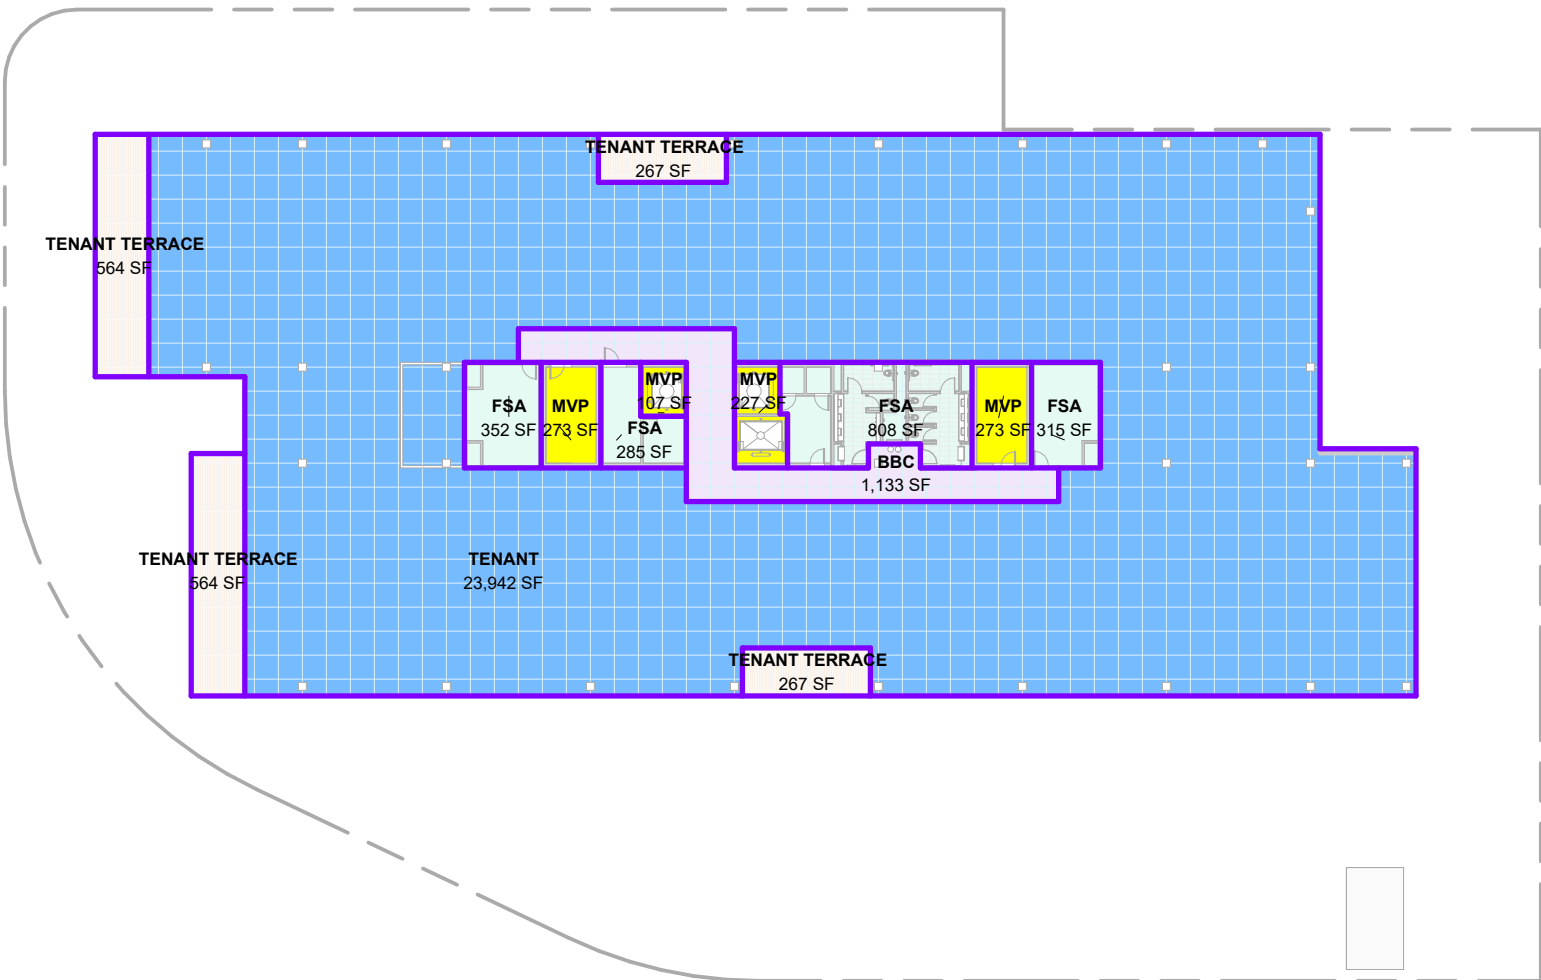

7 LEVEL 6 - OFFICE
1" = 40'-0"

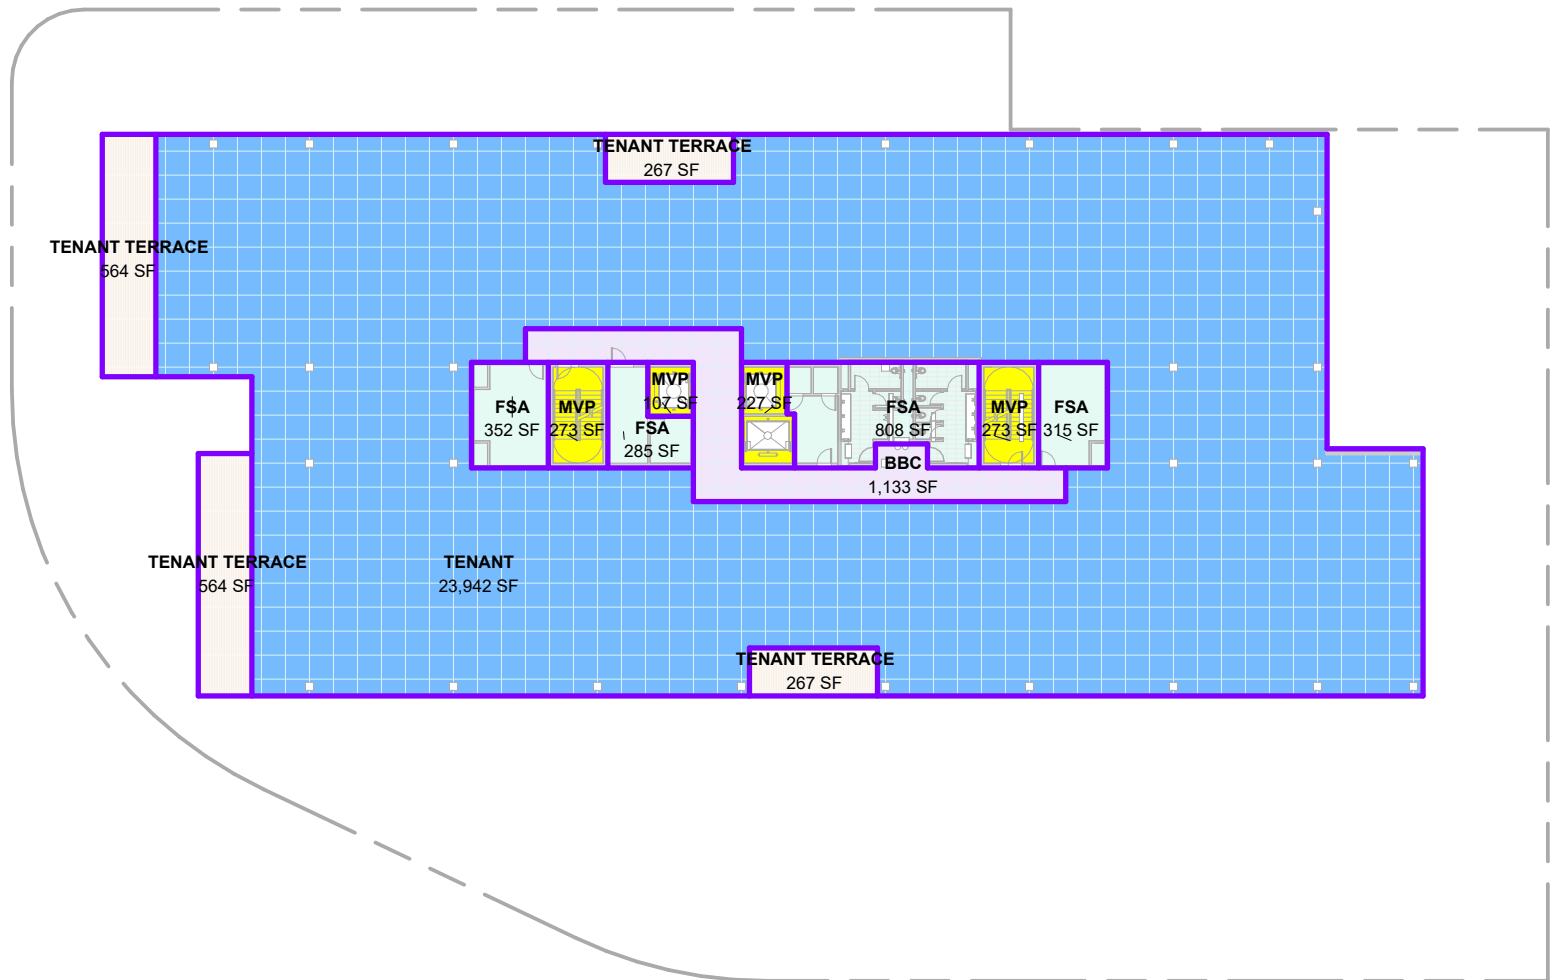

8 LEVEL 7 - OFFICE
1" = 40'-0"



9 LEVEL 08 - MECH ROOF
1" = 40'-0"

AREA SUMMARY

Area Schedule		
Level	Custom Area Type	Area
LEVEL 1 - LOBBY / RETAIL	BOH	114 SF
LEVEL 1 - LOBBY / RETAIL	Building Service Area	10,780 SF
LEVEL 1 - LOBBY / RETAIL	Lobby	4,753 SF
LEVEL 1 - LOBBY / RETAIL	Major Vertical Penetration	1,720 SF
LEVEL 1 - LOBBY / RETAIL	Parking	14,441 SF
LEVEL 1 - LOBBY / RETAIL	Retail	14,864 SF
LEVEL 1 - LOBBY / RETAIL		46,654 SF
LEVEL 2 - PARKING	Major Vertical Penetration	1,461 SF
LEVEL 2 - PARKING	Parking	22,028 SF
LEVEL 2 - PARKING		23,489 SF
LEVEL 2 - OFFICE	Major Vertical Penetration	328 SF
LEVEL 2 - OFFICE	Tenant Area	5,007 SF
LEVEL 2 - OFFICE	TENANT TERRACE	1,058 SF
LEVEL 2 - OFFICE		6,392 SF
LEVEL 3 - PARKING	Major Vertical Penetration	1,486 SF
LEVEL 3 - PARKING	Parking	36,443 SF
LEVEL 3 - PARKING		37,929 SF
LEVEL 4 - PARKING	Major Vertical Penetration	1,773 SF
LEVEL 4 - PARKING	PARKING	31,856 SF
LEVEL 4 - PARKING	Tenant Area	5,475 SF
LEVEL 4 - PARKING	Tenant Terrace	2,158 SF
LEVEL 4 - PARKING		41,262 SF
LEVEL 5 - OFFICE	Amenity	835 SF
LEVEL 5 - OFFICE	Base Building Circulation	1,240 SF
LEVEL 5 - OFFICE	Floor Service Area	2,354 SF
LEVEL 5 - OFFICE	Major Vertical Penetration	1,199 SF
LEVEL 5 - OFFICE	Tenant Area	22,359 SF
LEVEL 5 - OFFICE	Tenant Terrace	2,689 SF
LEVEL 5 - OFFICE		30,677 SF
LEVEL 6 - OFFICE	Base Building Circulation	1,133 SF
LEVEL 6 - OFFICE	Floor Service Area	1,761 SF
LEVEL 6 - OFFICE	Major Vertical Penetration	880 SF
LEVEL 6 - OFFICE	Tenant Area	23,942 SF
LEVEL 6 - OFFICE	Tenant Terrace	1,661 SF
LEVEL 6 - OFFICE		29,376 SF
LEVEL 7 - OFFICE	Base Building Circulation	1,133 SF
LEVEL 7 - OFFICE	Floor Service Area	1,761 SF
LEVEL 7 - OFFICE	Major Vertical Penetration	880 SF
LEVEL 7 - OFFICE	Tenant Area	23,942 SF
LEVEL 7 - OFFICE	Tenant Terrace	1,661 SF
LEVEL 7 - OFFICE		29,376 SF
LEVEL 08 - MECH ROOF	Building Service Area	401 SF
LEVEL 08 - MECH ROOF	Major Vertical Penetration	737 SF
LEVEL 08 - MECH ROOF		1,138 SF
		246,292 SF

Charleston Magnolia

115 Bachman Boulevard
Charleston, SC 29405

Owner
Highland Resources, Inc.
2198 Milford Street
Charleston, South Carolina 29405
tel. 713.358.2370 fax. 713.655.1344
www.highlandresourcesinc.com

Design Consultant
Pickard Chilton
980 Chapel Street
New Haven, Connecticut 06510
tel. 203.758-8000 fax. 203.786.8610
www.pickardchilton.com

Architect of Record
Cooper Carry
625 North Washington Street, Suite 200
Alexandria, Virginia 22314
tel. 703.519.6152 fax. 703.519.7127
www.coopercarry.com

Landscape Architect
Design Works
334 East Bay Street #240
Charleston, South Carolina 29401
tel. 843.723.5525
www.designworkslc.com

Structural Engineer
Britt, Peters & Associates, Inc.
101 Falls Park Drive, Suite 601
Greenville, South Carolina 29601
tel. 843.271.8869
www.brittpeters.com

Mechanical and Electrical Engineer
Barrett, Woodyard & Associates
420 Minuet Lane
Charlotte, North Carolina 28217
tel. 704.357.9333
www.barrettwoodyard.com

Civil Engineer
Reveer Group
2971 West Montague Avenue, Suite 101
North Charleston, South Carolina 29418
tel. 843.297.4103
https://www.reveergroup.com/


REVISIONS

CURTAIN WALL RFP

This drawing is not for construction or bidding purposes. Pickard Chilton Architects, Inc. has prepared this drawing solely to communicate architectural design intent. Pickard Chilton Architects, Inc. is not the Architect of Record and therefore is not responsible for preparing construction documents or for technical, legal, or construction-related matters. Pickard Chilton Architects, Inc. is not responsible for nor does it make any representation concerning dimensional accuracy of this drawing or coordination of this drawing with documents prepared by other disciplines.

NOT FOR CONSTRUCTION

AREA AND PARKING SUMMARY

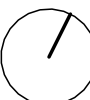

PROJECT: 2308
DATE: 07 APRIL 2026
SCALE: 1" = 40'-0"

SHEET
NUMBER:

A0.03

Copyright 2026 by Pickard Chilton Architects, Inc. All rights reserved.