
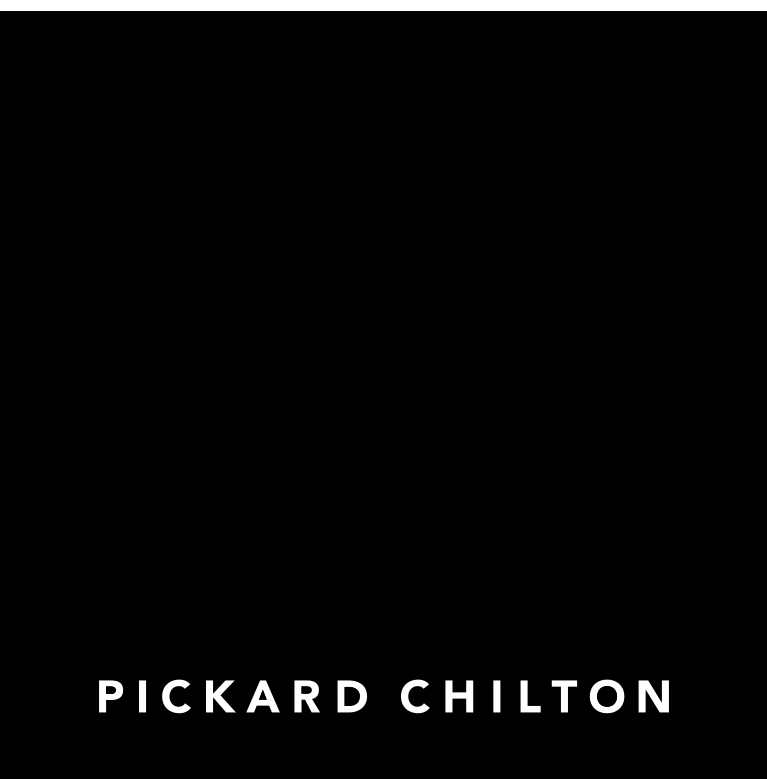


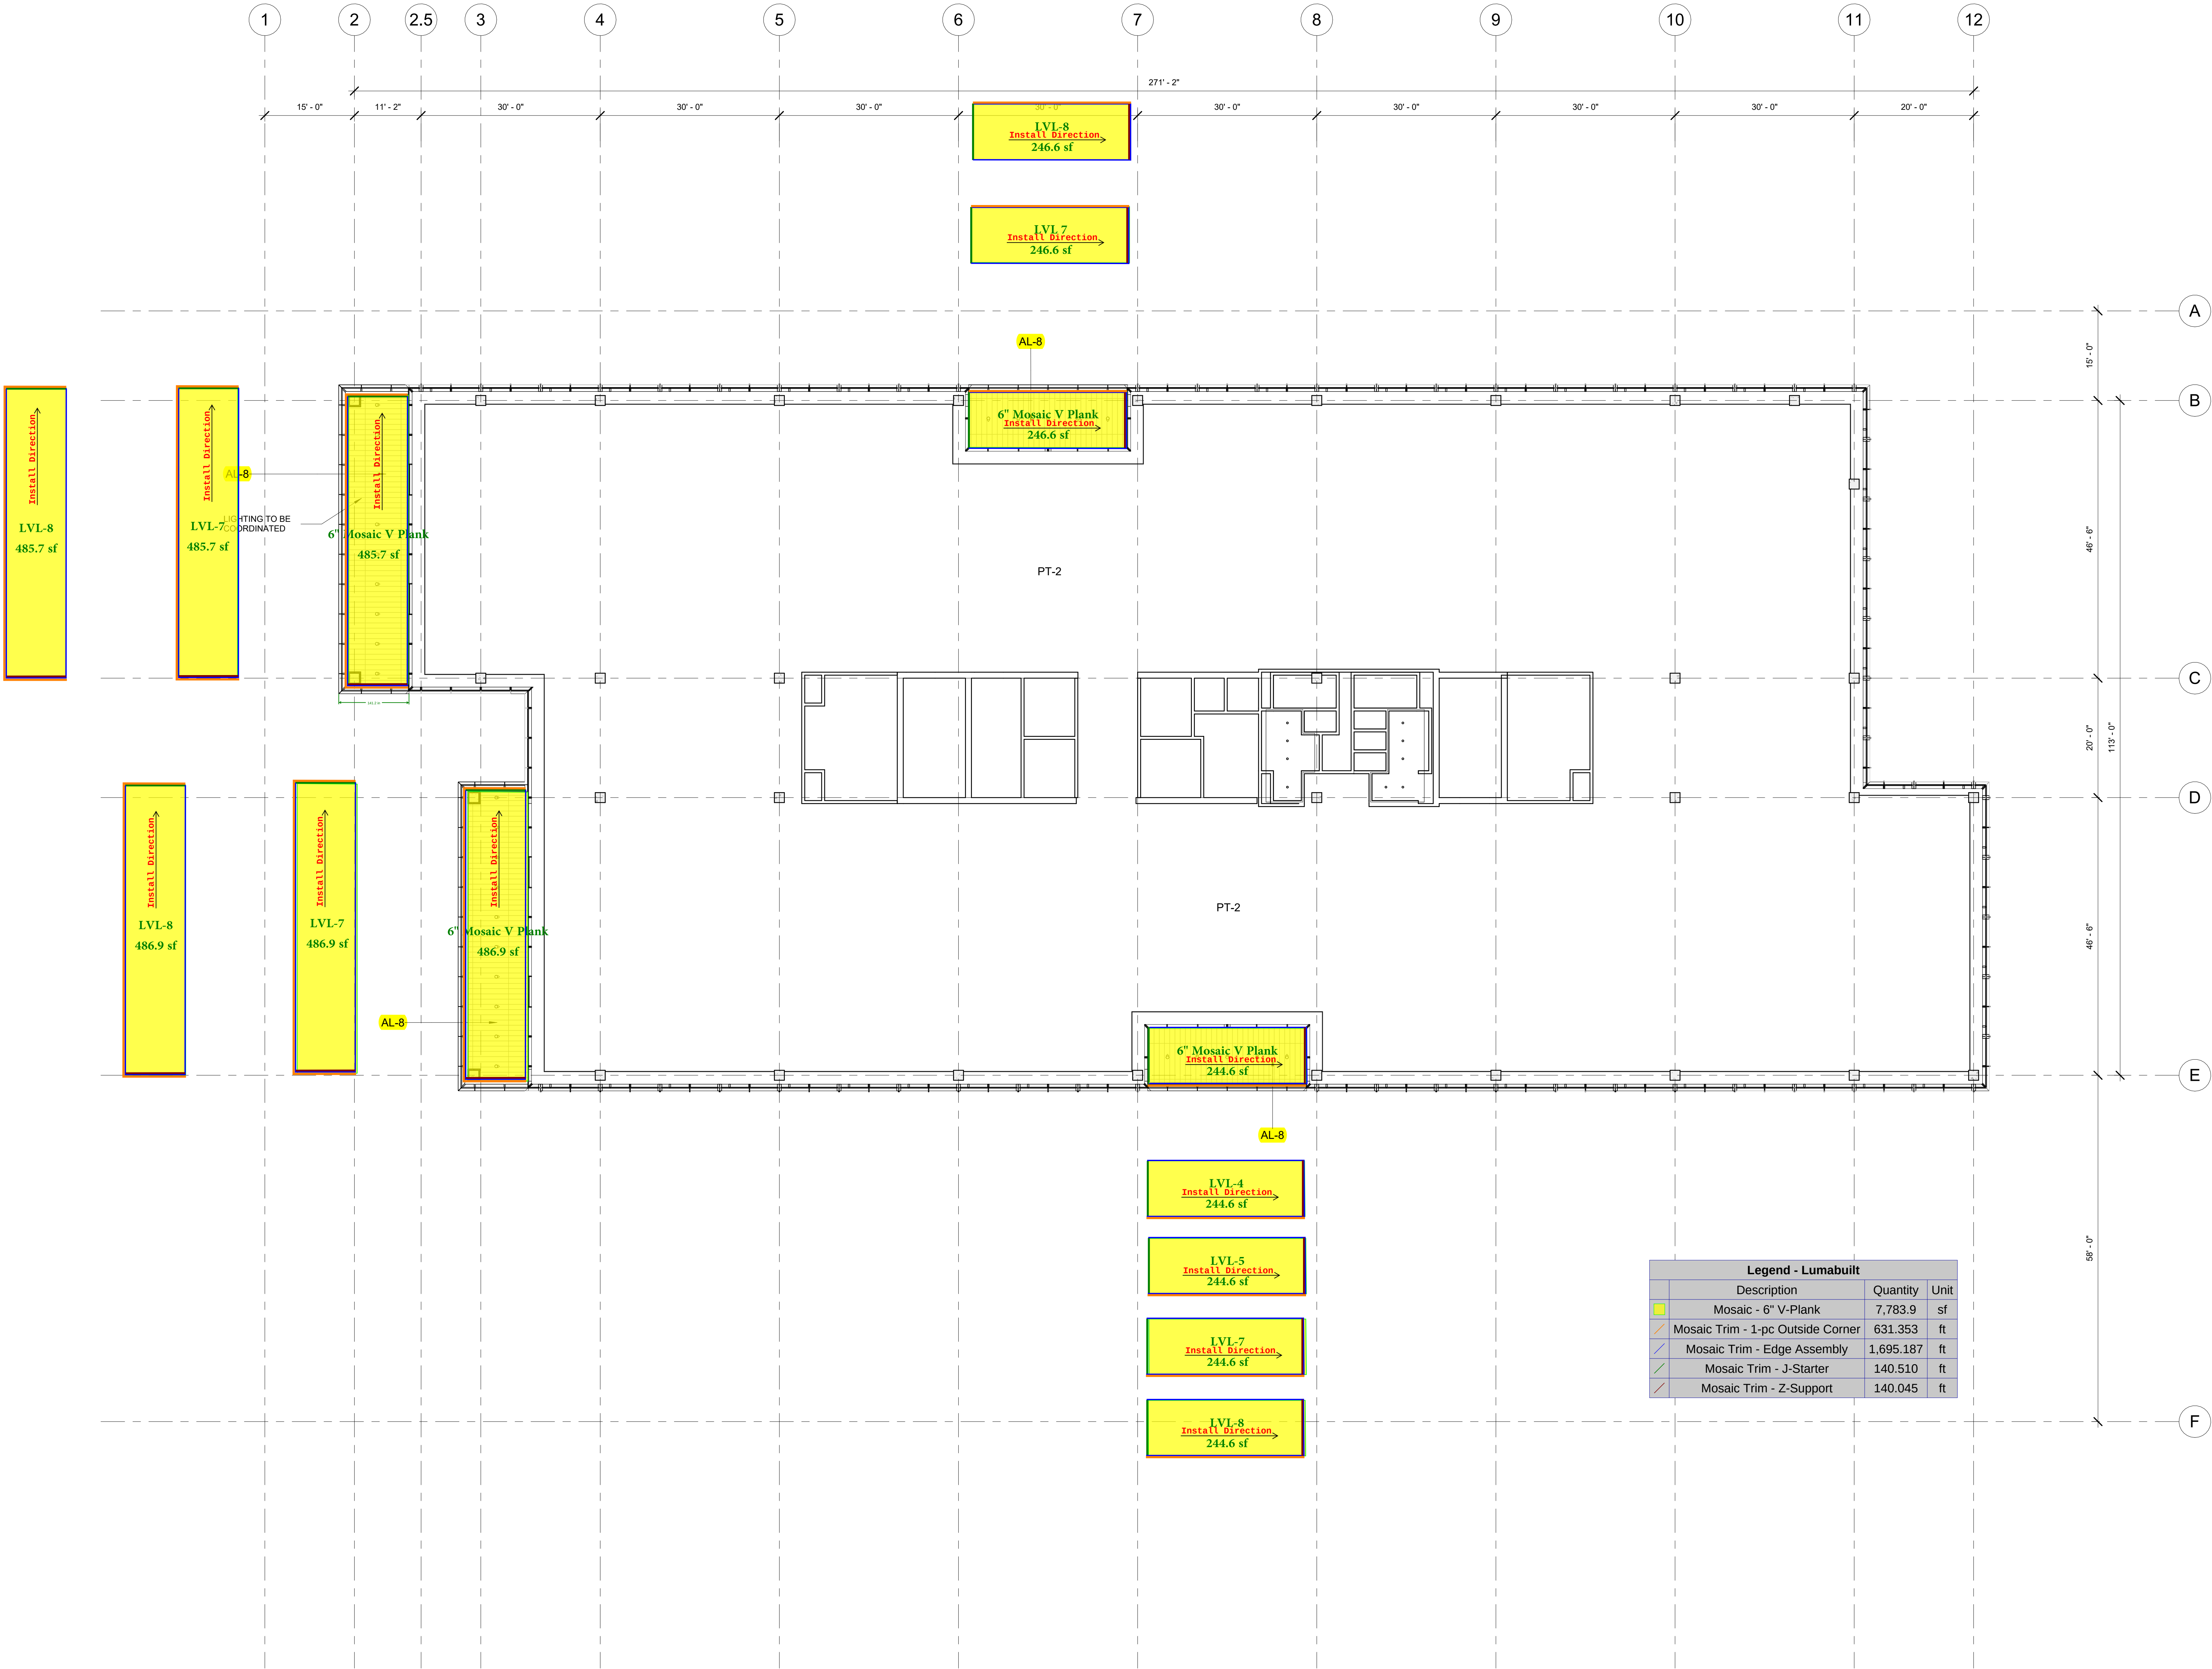

Charleston Magnolia
115 Bachman Boulevard
Charleston, SC 29405

Owner
Highland Resources, Inc.
2188 Milford Street
Charleston, South Carolina 29405
tel. 713.358.2370 fax. 713.655.1344
www.highlandresourcesinc.com

Design Consultant
Pickard Chilton
980 Chapel Street
New Haven, Connecticut 06510
tel. 203.786-8000 fax. 203.786.8610
www.pickardchilton.com

Architect of Record
Cooper Carry
625 North Washington Street, Suite 200
Alexandria, Virginia 22314
tel. 703.519.6152 fax. 703.519.7127
www.coopercarry.com

Landscape Architect
Design Works
334 East Bay Street #240
Charleston, South Carolina 29401
tel. 843.723.6525
www.designworksllc.com

Structural Engineer
Britt, Peters & Associates, Inc.
101 Falls Park Drive, Suite 601
Greenville, South Carolina 29601
tel. 864.271.8869
www.brittpeters.com

Mechanical and Electrical Engineer
Barrett, Woodyard & Associates
420 Minuet Lane
Charlotte, North Carolina 28217
tel. 704.357.9333
www.barrettwoodyard.com

Civil Engineer
Reveer Group
2971 West Montague Avenue, Suite 101
North Charleston, South Carolina 29418
tel. 843.297.4103
https://www.reveergroup.com/

REVISIONS

CURTAIN WALL RFP

This drawing is not for construction or bidding purposes. Pickard Chilton Architects, Inc. has prepared this drawing solely to communicate architectural design intent. Pickard Chilton Architects, Inc. is not the Architect of Record and therefore is not responsible for preparing construction documents or for technical, legal, or construction-related matters. Pickard Chilton Architects, Inc. is not responsible for nor does it make any representation concerning dimensional accuracy of this drawing or coordination of this drawing with documents prepared by other disciplines.

NOT FOR CONSTRUCTION

LEVEL 6 RCP - OFFICE

PROJECT: 2308
DATE: 07 APRIL 2026
SCALE: 3/32" = 1'-0"

SHEET
NUMBER:
A8.06

Copyright 2026 by Pickard Chilton Architects, Inc. All rights reserved.